PLAN SHOWING THE PROPOSED CONSTRUCTION OF A TERRACE ROOF SHOP BUILDING IN RE.SY.NO: 109 / 3A2 OF VALVACHAGOSTAM 'A' VILLAGE, VALVACHAGOSTAM TOWN PANCHAYAT , KALKULAM TALUK, K.K.DISTRICT.

N


NAME OF OWNER:

Mrs.SUSELA.P,
W/O.Mr.VINCENT,
KURAVANVILAI,
KAVIYALOOR,
KATTATHURAI POST,
K.K.DIST, TAMILNADU - 629158.


AREA DETAILS - BUILDING		
PLINTH AREA		
Plinth Area	21.50 Sq.m	231.43 Sq.ft
Floor Area	18.13 Sq.m	195.15 Sq.ft
AREA DETAILS - PLOT		
Site Area	1.334 Cents	0.54 Are
	(53.987 Sq.m)	(581.09 Sq.ft)
Vacant Area	32.49 Sq.m	349.69 Sq.ft
F.S.I	21.50 / 53.99	0.40 < 2.00
PC	21.50 / 53.99	39.82 < 50

SIGNATURE OF OWNER


SIGNATURE OF ENGINEER

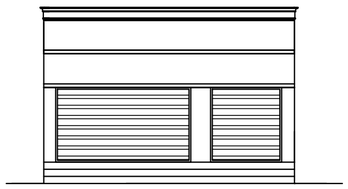


ELEVATION

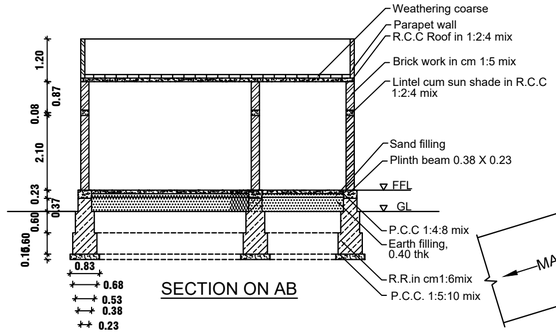


SECTION ON AB

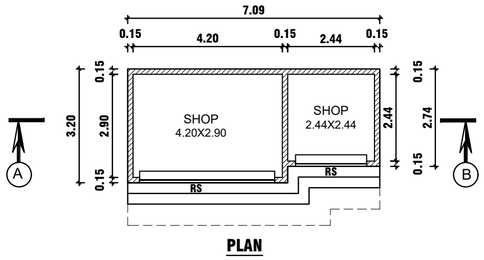


PLAN

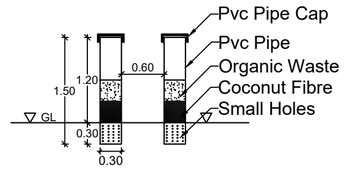


PIPE COMPOST PIT

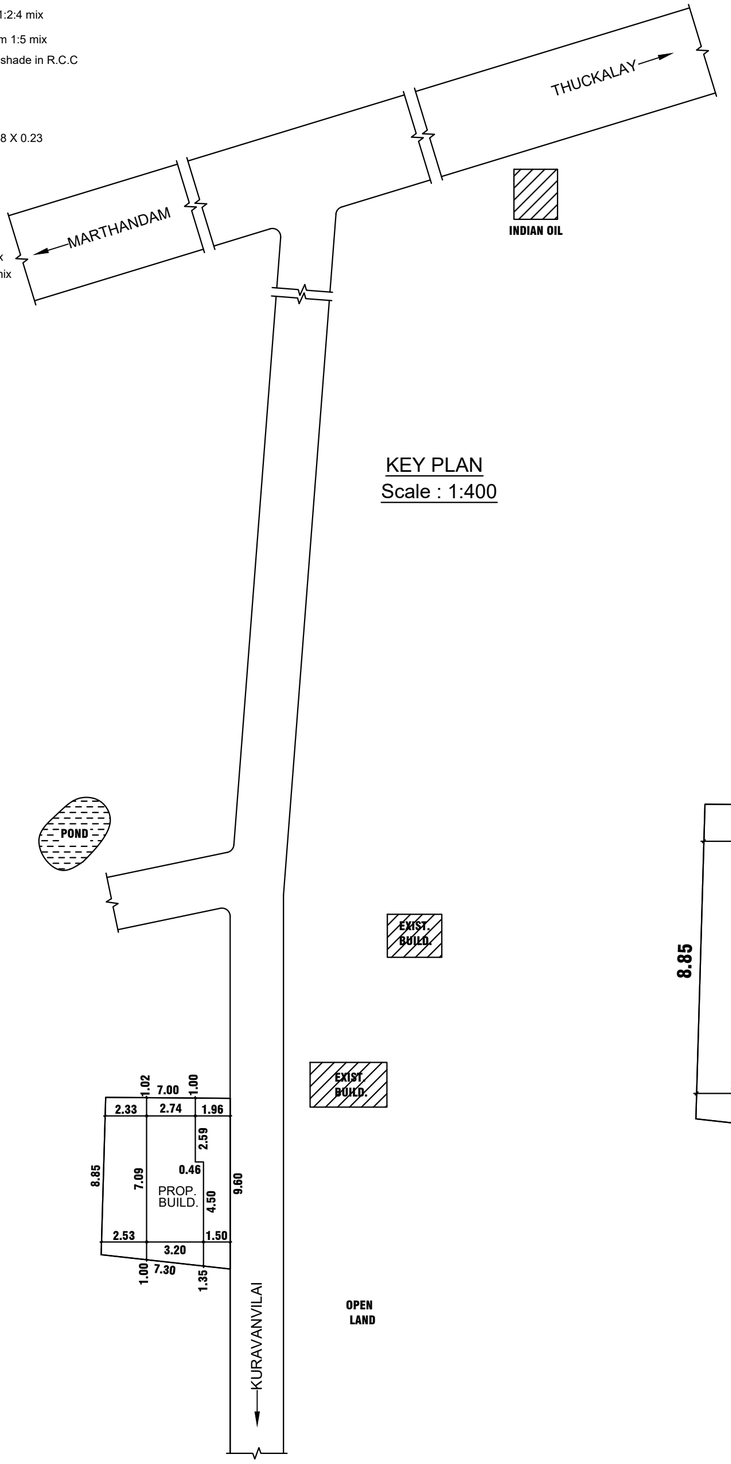


KEY PLAN
Scale : 1:400

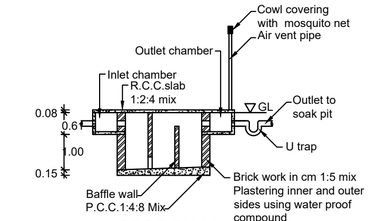


SECTION UV

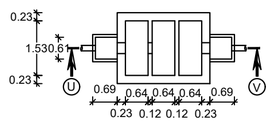


SEPTIC TANK PLAN

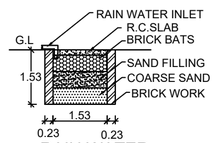


RAIN WATER
HARVESTING PIT

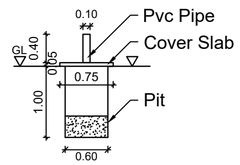


SOLID WASTE COMPOST PIT

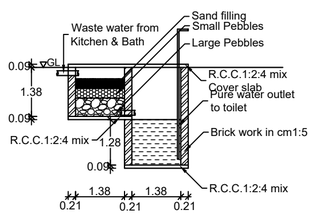

WASTE WATER RECYCLING SYSTEM

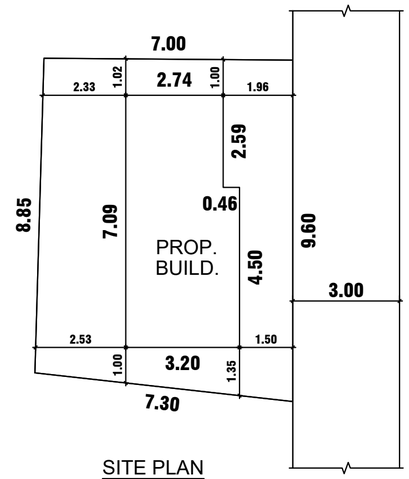

SITE PLAN
Scale : 1:100

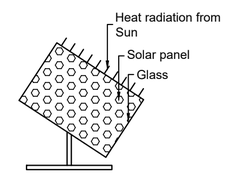

SOLAR SYSTEM

SCHEDULE OF JOINERIES		
REF	DESCRIPTION	SIZE
RS	ROLLING SHUTTER	3.80 X 2.10
D1	DOOR	0.80 X 2.10

SCHEDULE OF JOINERIES		
RS	ROLLING SHUTTER	0.20X 2.10
V	VENTILATOR	0.90 X 0.60

Er.JEGAN LAL

SHIYA CONSTRUCTIONS

ANANDHA KRISHNAN COMPLEX,
ARUMANAI JUNCTION-629151
MOBILE NO:6379939099
email:jegansurvey1991.jl@gmail.com

SCALE : 1:100

ALL DIMENSIONS ARE IN METRE

DWG NO 911 09 2026