

PLAN SHOWING THE PROPOSED CONSTRUCTION OF A TERRACE ROOF RESIDENTIAL BUILDING IN RE.SY.NO:413 / 11B OF THUMBACODE "B" VILLAGE IN THIRPARAPPU TOWN PANCHAYAT, THIRUVATTAR TALUK,K.K.DISTRICT .

NAME OF OWNER:
Mr.U.S.VISHNU PRAKASH,
S/O Mr.UNNI KRISHNAN,
KONIKUTTI VILAI, THUMBACODE,
KULASEKHARAM & P.O.,
K.K.DISTRICT .

SIGNATURE:



Design By:




MAMOODE JN,
KULASEKARAM
Cell:9944128380,
9443160923.,

REFERENCE


PRO.BUILDING
EXT.BUILDING
ROAD
SITE

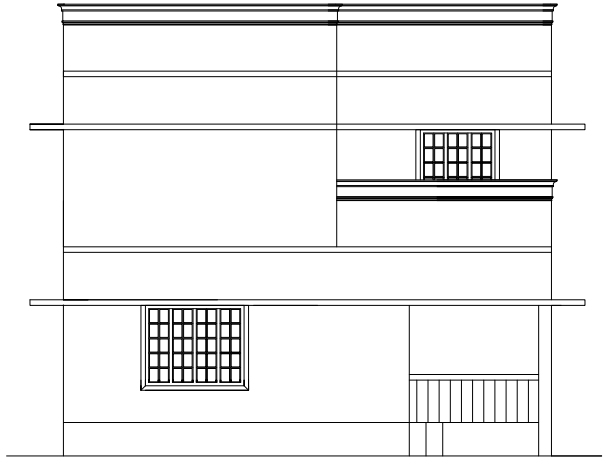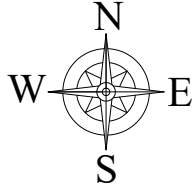

ELEVATION

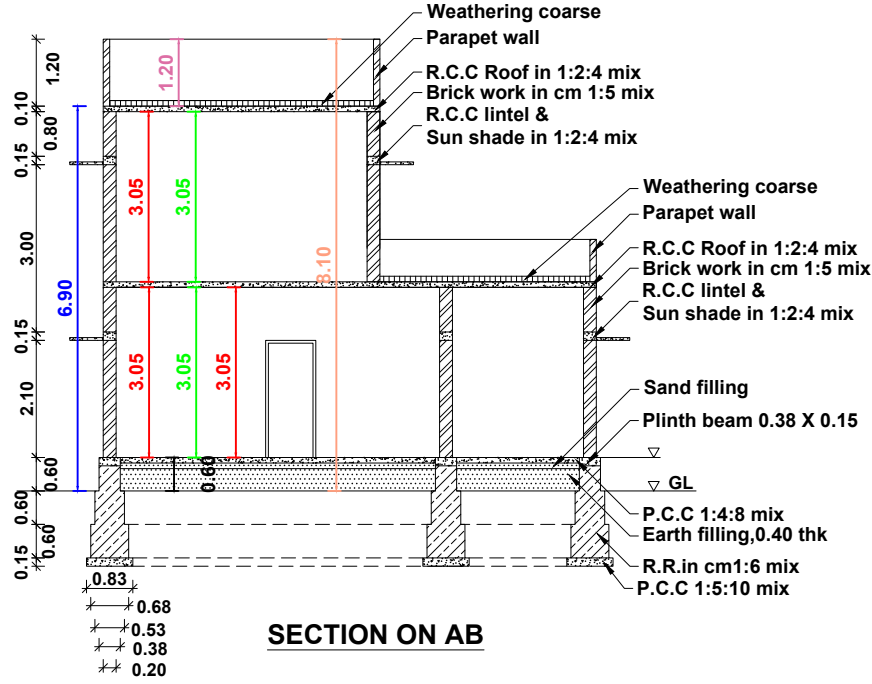


SECTION ON AB

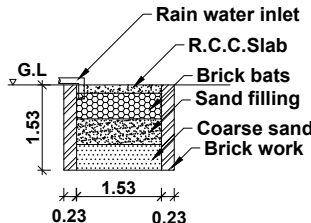


RAIN WATER
HARVESTING PIT

PLAN INFO
PLOT AREA_M2=343.99
AS_AT_SITE=348.92
FMB_OR_PLR=343.99
AS_PER_DOCUMENT=343.99
ROAD_WIDTH=4.50
AVG_PLOT_WIDTH=13.00
AVG_PLOT_DEPTH=30.00
ROAD_LENGTH=100.00
AREA_TYPE=OTHERS
SURVEY_NO=413/11B
PATTA_NO=9489
TALUK=THIRUVATTAR
JURISDICTION_TYPE=PANCHAYAT
SINGLE_FAMILY_BLDG=YES
OSR_APPLICABLE=NO
OSR_SURR_BUYBACK_RETAIN=RETAIN
PREMIUM_FSI_REQUIRED=NO
OSR_SURRENDER_OR_BUYBACK=YES
IS_APPROVED_LAYOUT=YES
ORGANIZATION_TYPE=PRIVATE
CRZ=NO
LAND_USE_ZONE = RESIDENTIAL
PLOT_NO=0
DISTRICT=KANYAKUMARI
IS_SWIMMING_POOL_EXISTS=NO
RWH_DECLARED=YES
IF_HERITAGE_TOWN_LESS THAN 1KM_RADIUS=NO

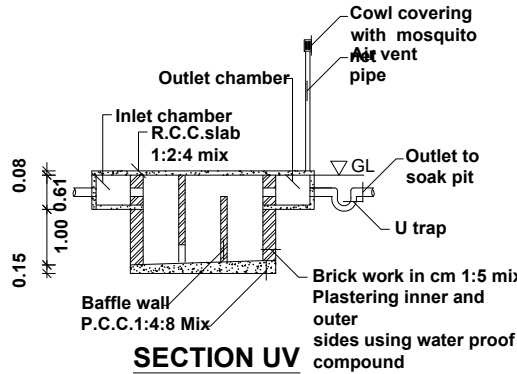

SECTION UV

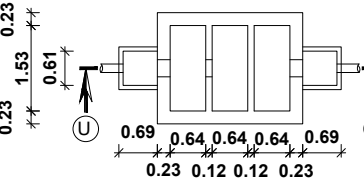

SEPTIC TANK PLAN

Parking calculation As per TNCDB Rules 2019- Annexure IV/Part 1(1)Residential/(B)
Dwelling Unit with Floor area above 100 sq.m, Number of Parking Spaces=1 car space for every 100 sq.m
Total Floor Area =205.41 Sq.m
Required number of car parking spaces:205.41 / 100=2.05 no
Provided number of car parking spaces: 3 nos

AREA DETAILS - BUILDING

PLINTH AREA		
Ground Floor	103.56 Sq.m	1114.72 Sq.ft
First Floor	101.85 Sq.m	1096.31 Sq.ft
Total	205.41 Sq.m	2211.03 Sq.ft

FLOOR AREA		
Ground Floor	88.63 Sq.m	954.01 Sq.ft
First Floor	87.05 Sq.m	937.01 Sq.ft
Total	175.68 Sq.m	1891.02 Sq.ft

AREA DETAILS - PLOT

Site Area	8.500 Cents	3.44 Are
	(343.995 Sq.m)	(3702.60 Sq.ft)
Vacant Area	240.44 Sq.m	2588.04 Sq.ft
F.S.I	205.41 / 344.00	0.60 < 2.00
PC	103.56 / 344.00	30.11 < 50


SCHEDULE OF JOINERIES

REF	DESCRIPTION	SIZE
D	DOOR	0.90X2.10
D1	DOOR	0.80X2.10
W3	WINDOW	1.50X1.50
W2	WINDOW	0.90X1.50
KW2	WINDOW	0.90X1.00
V	VENTILATOR	0.90X0.60


SCALE : 1:100	ALL DIMENSIONS ARE IN METRE	Dwg.No: 20260919
------------------	--------------------------------	---------------------

H.G. Williams


H.G. WILLIAMS DC
Reg. Engineer Grade-III
Reg. No: RE-III/KK DTCP/17/2024
WILLIAMS CONSTRUCTIONS
THIRUVATTAR
Phone: 04651-282412
ENGINEER

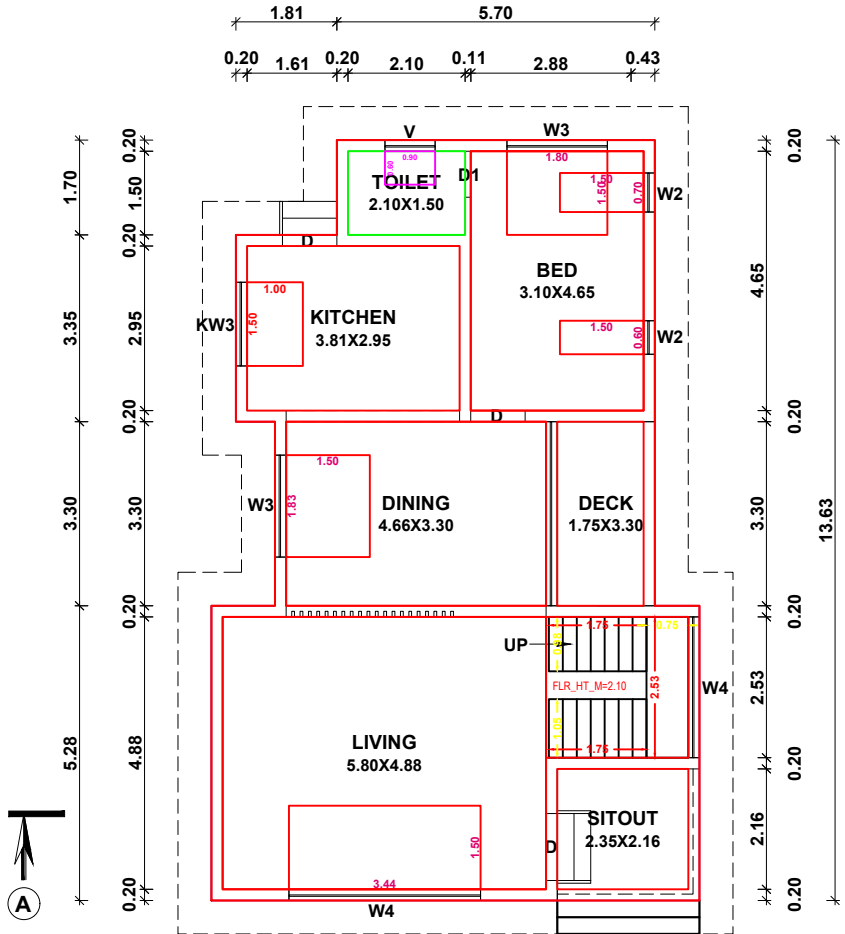


GROUND FLOOR PLAN

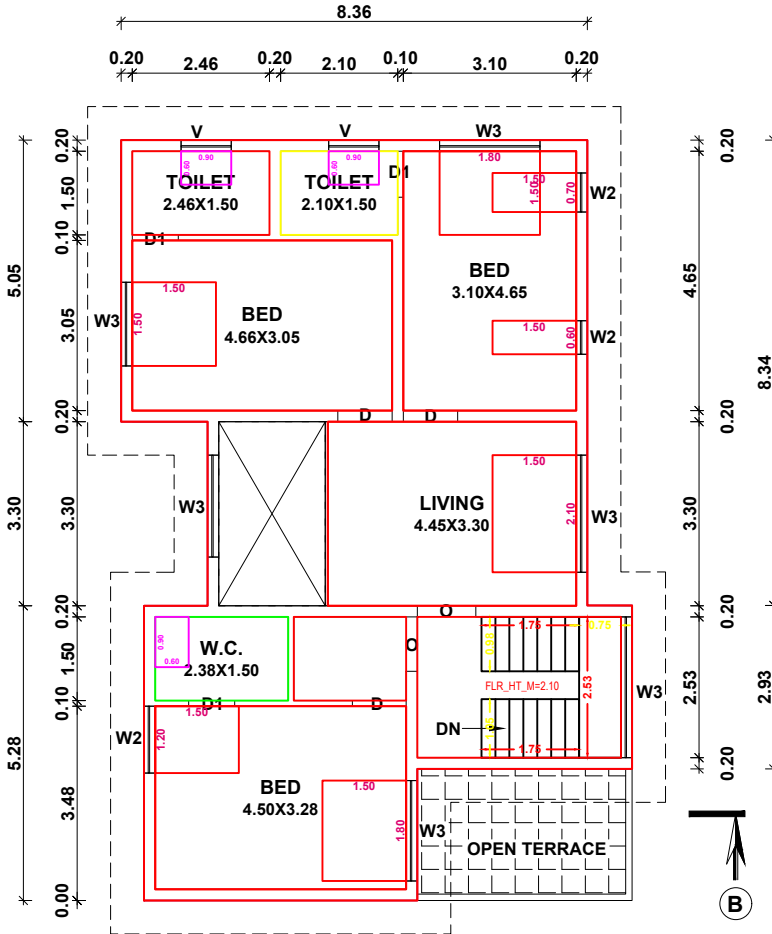


FIRST FLOOR PLAN

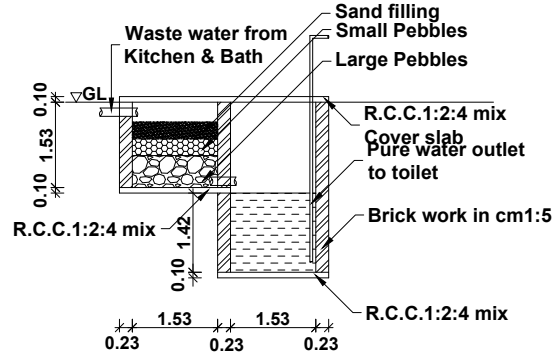


WASTE WATER RECYCLING SYSTEM

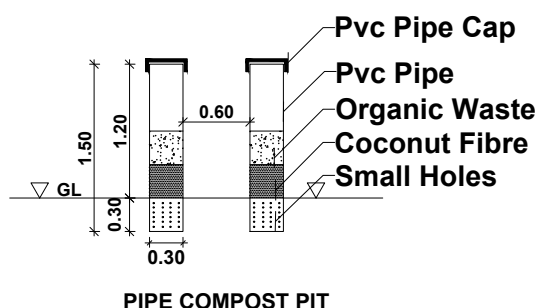


PIPE COMPOST PIT

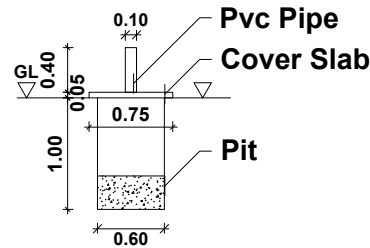


SOLID WASTE COMPOST PIT

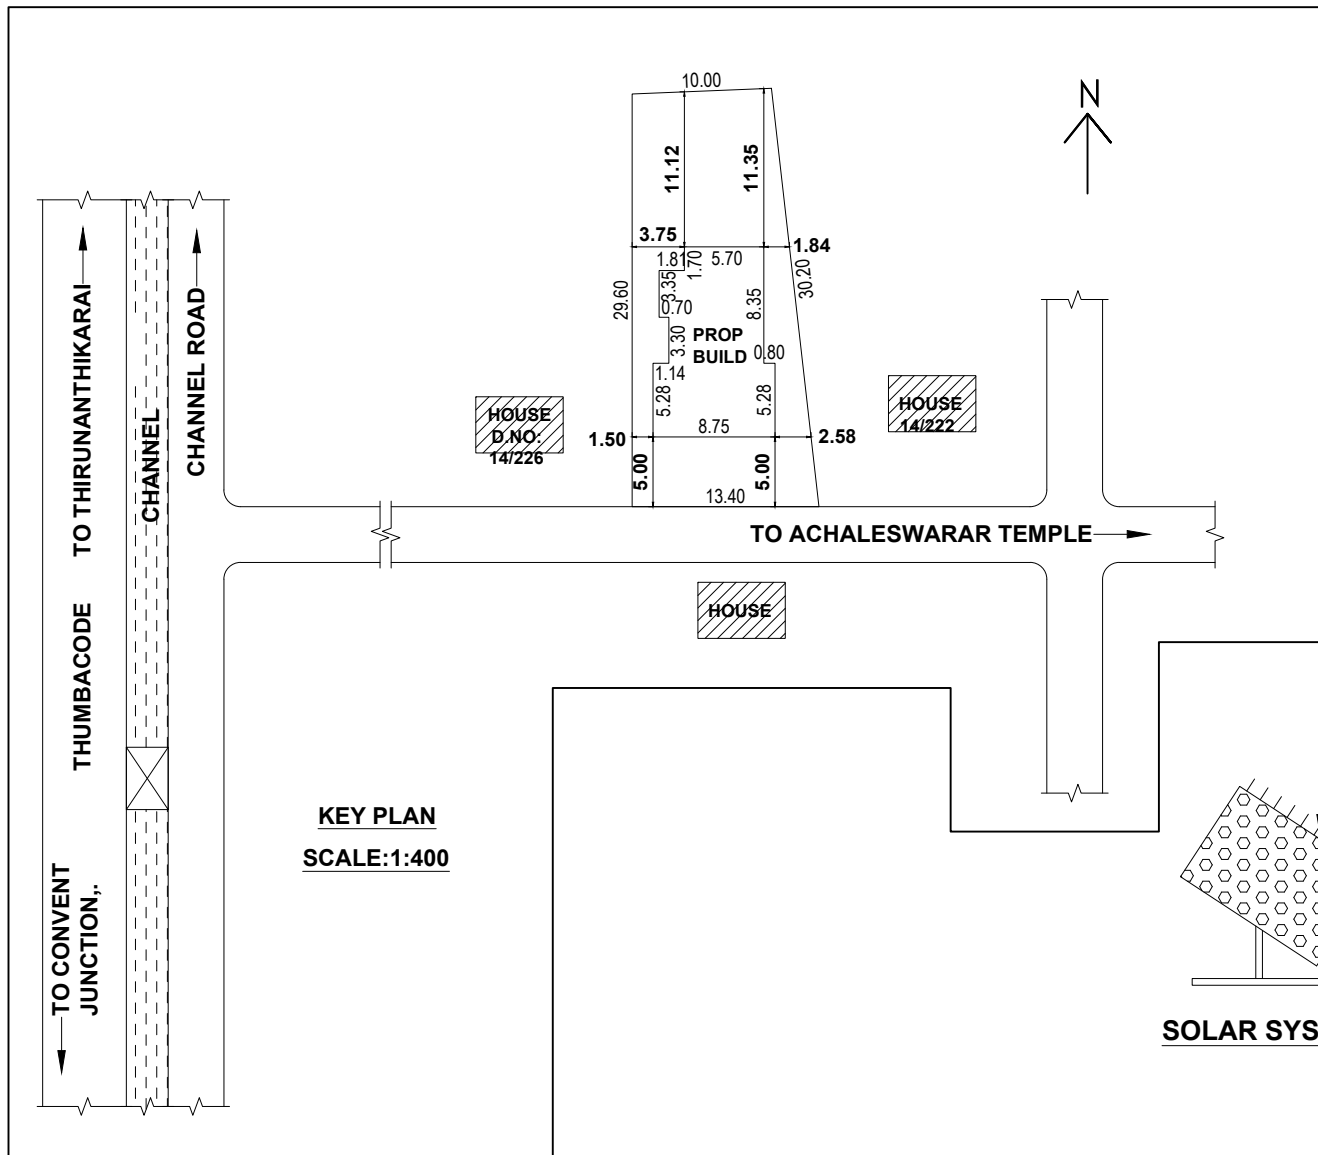

KEY PLAN
SCALE:1:400

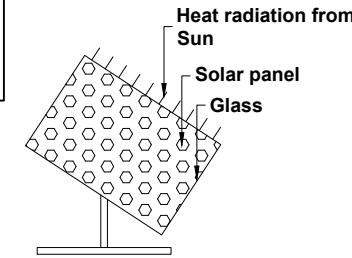

SOLAR SYSTEM

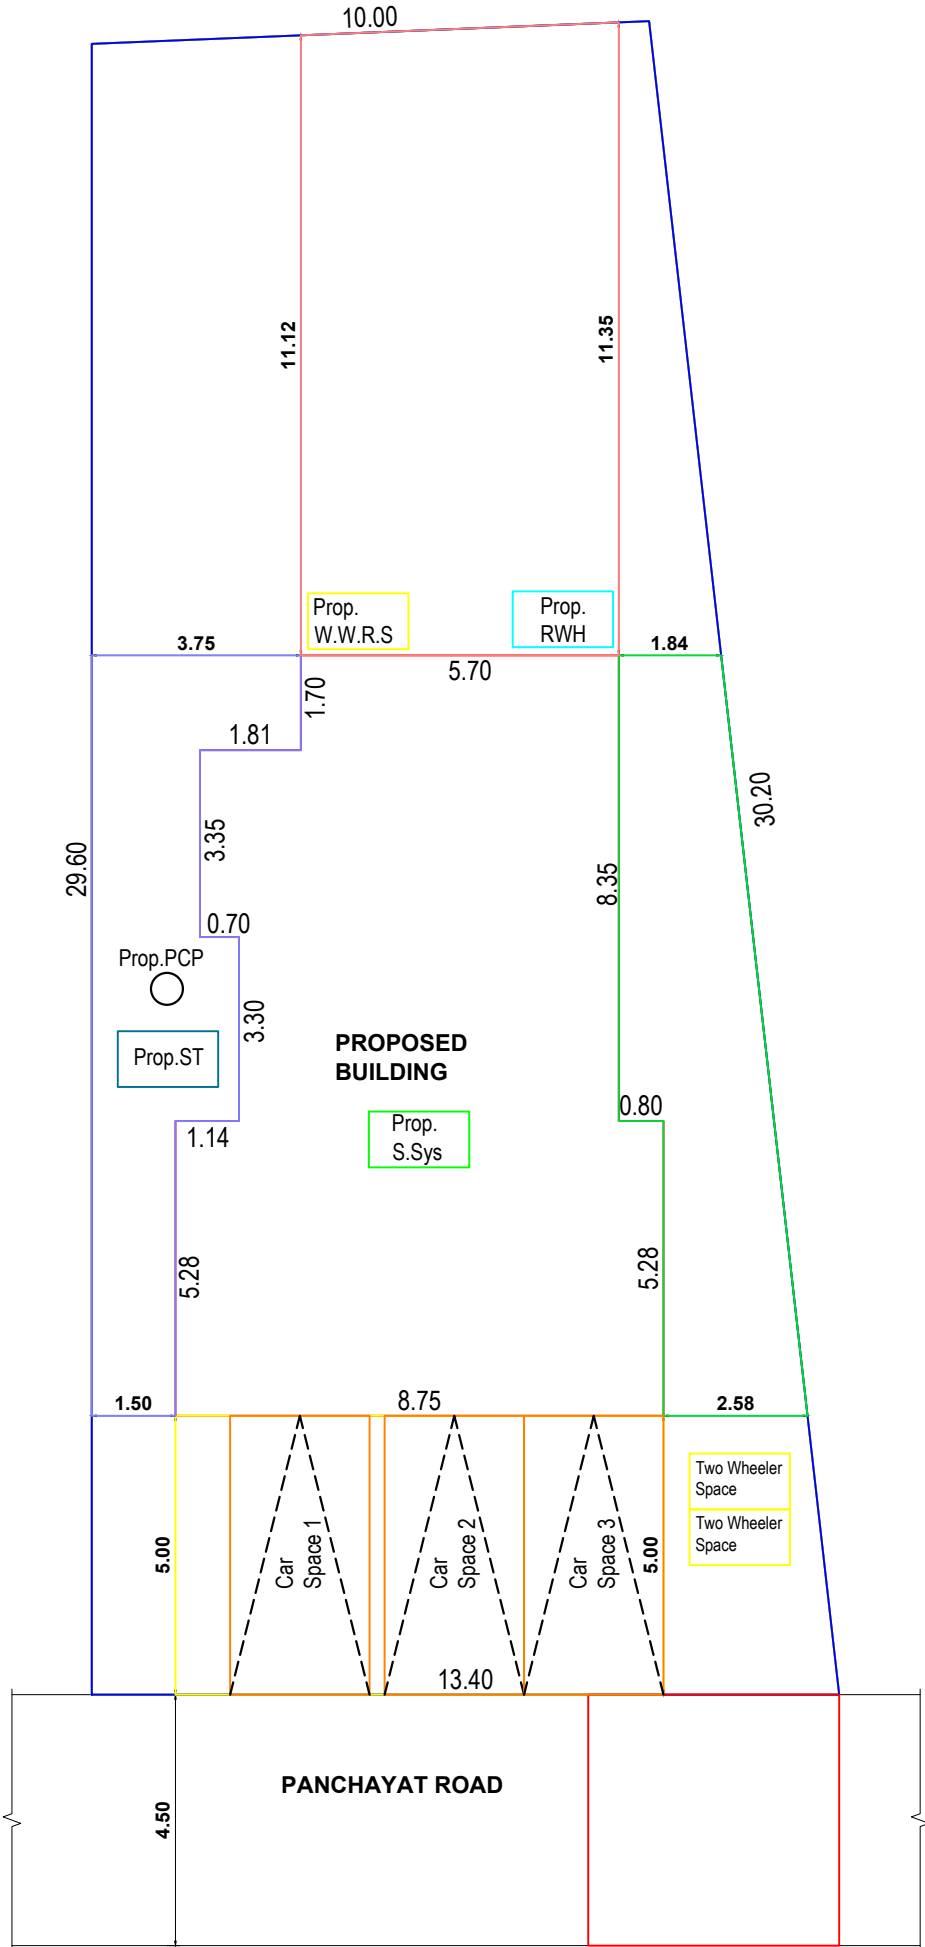

SITE PLAN
SCALE:1:100