
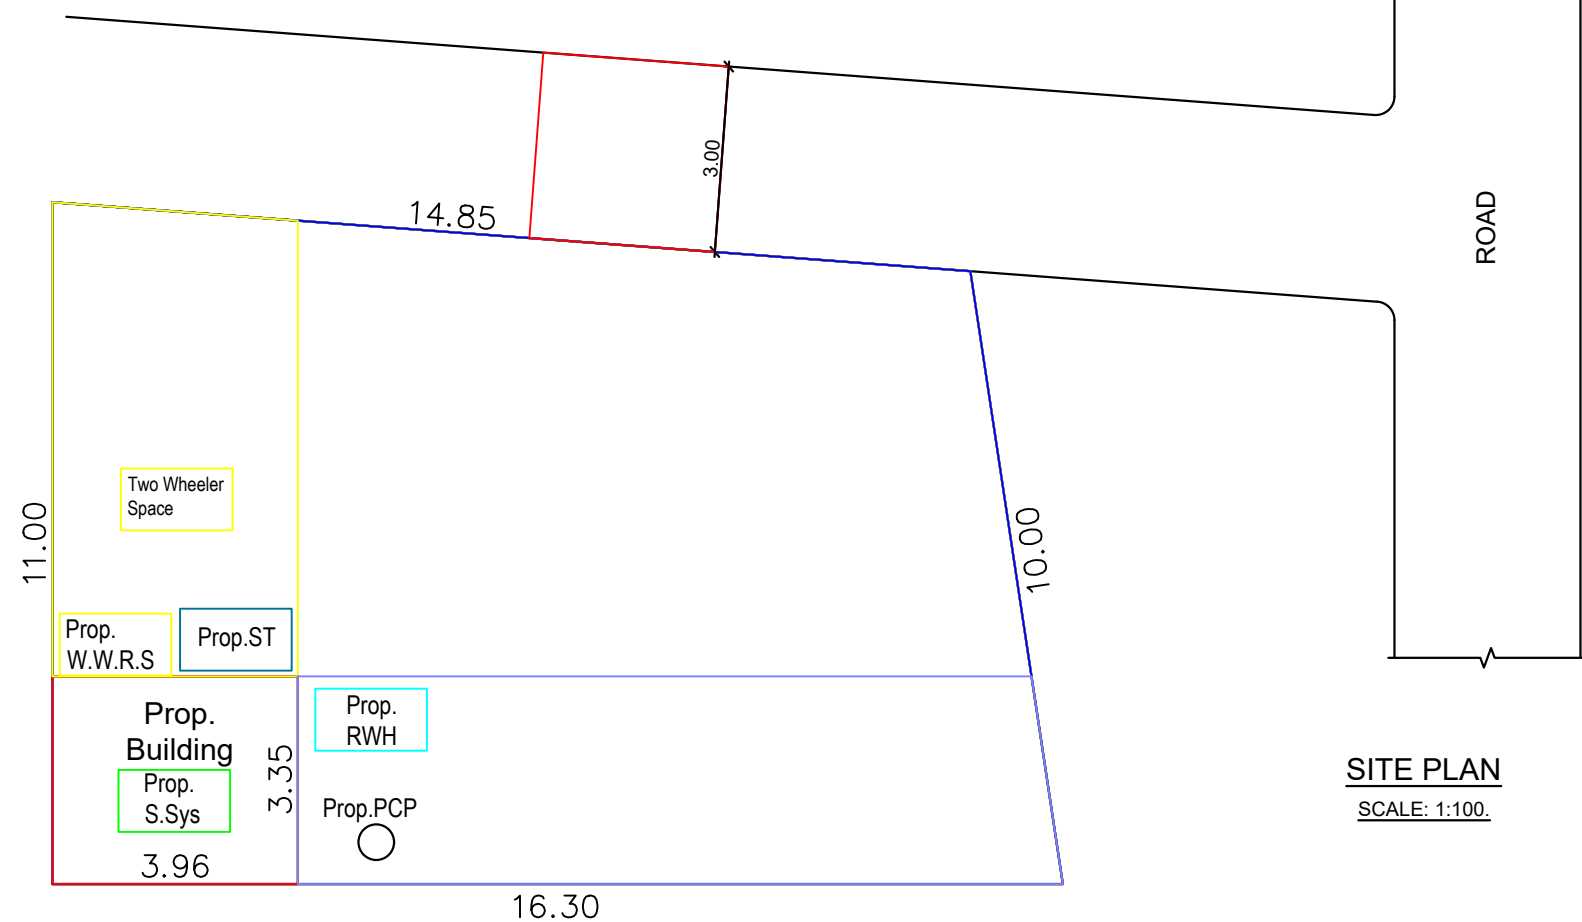
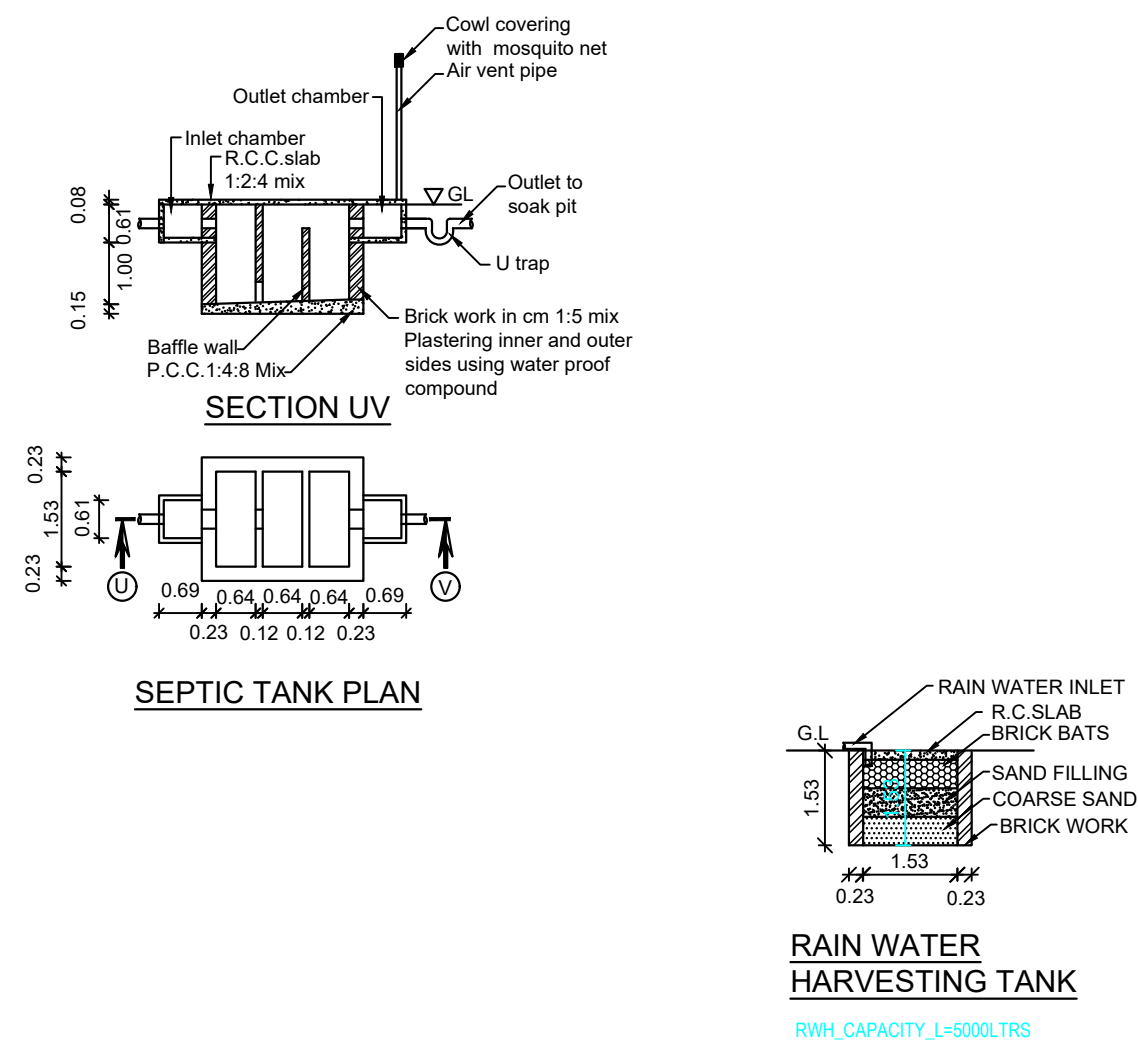
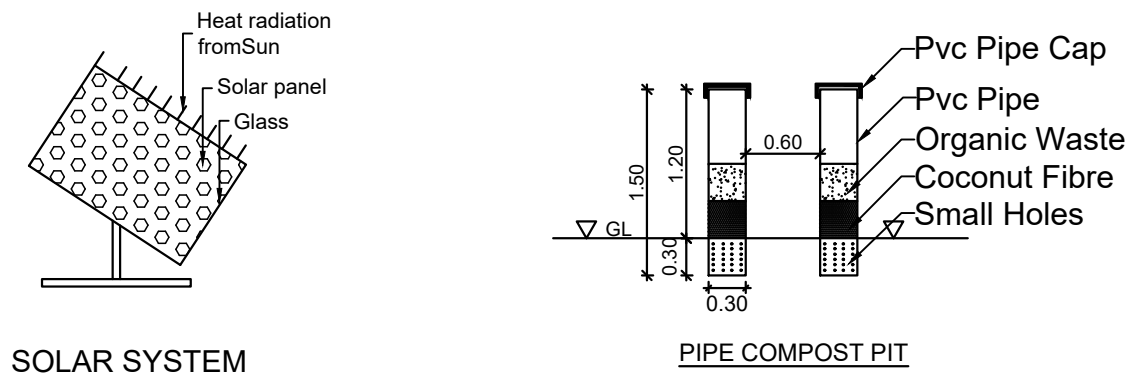
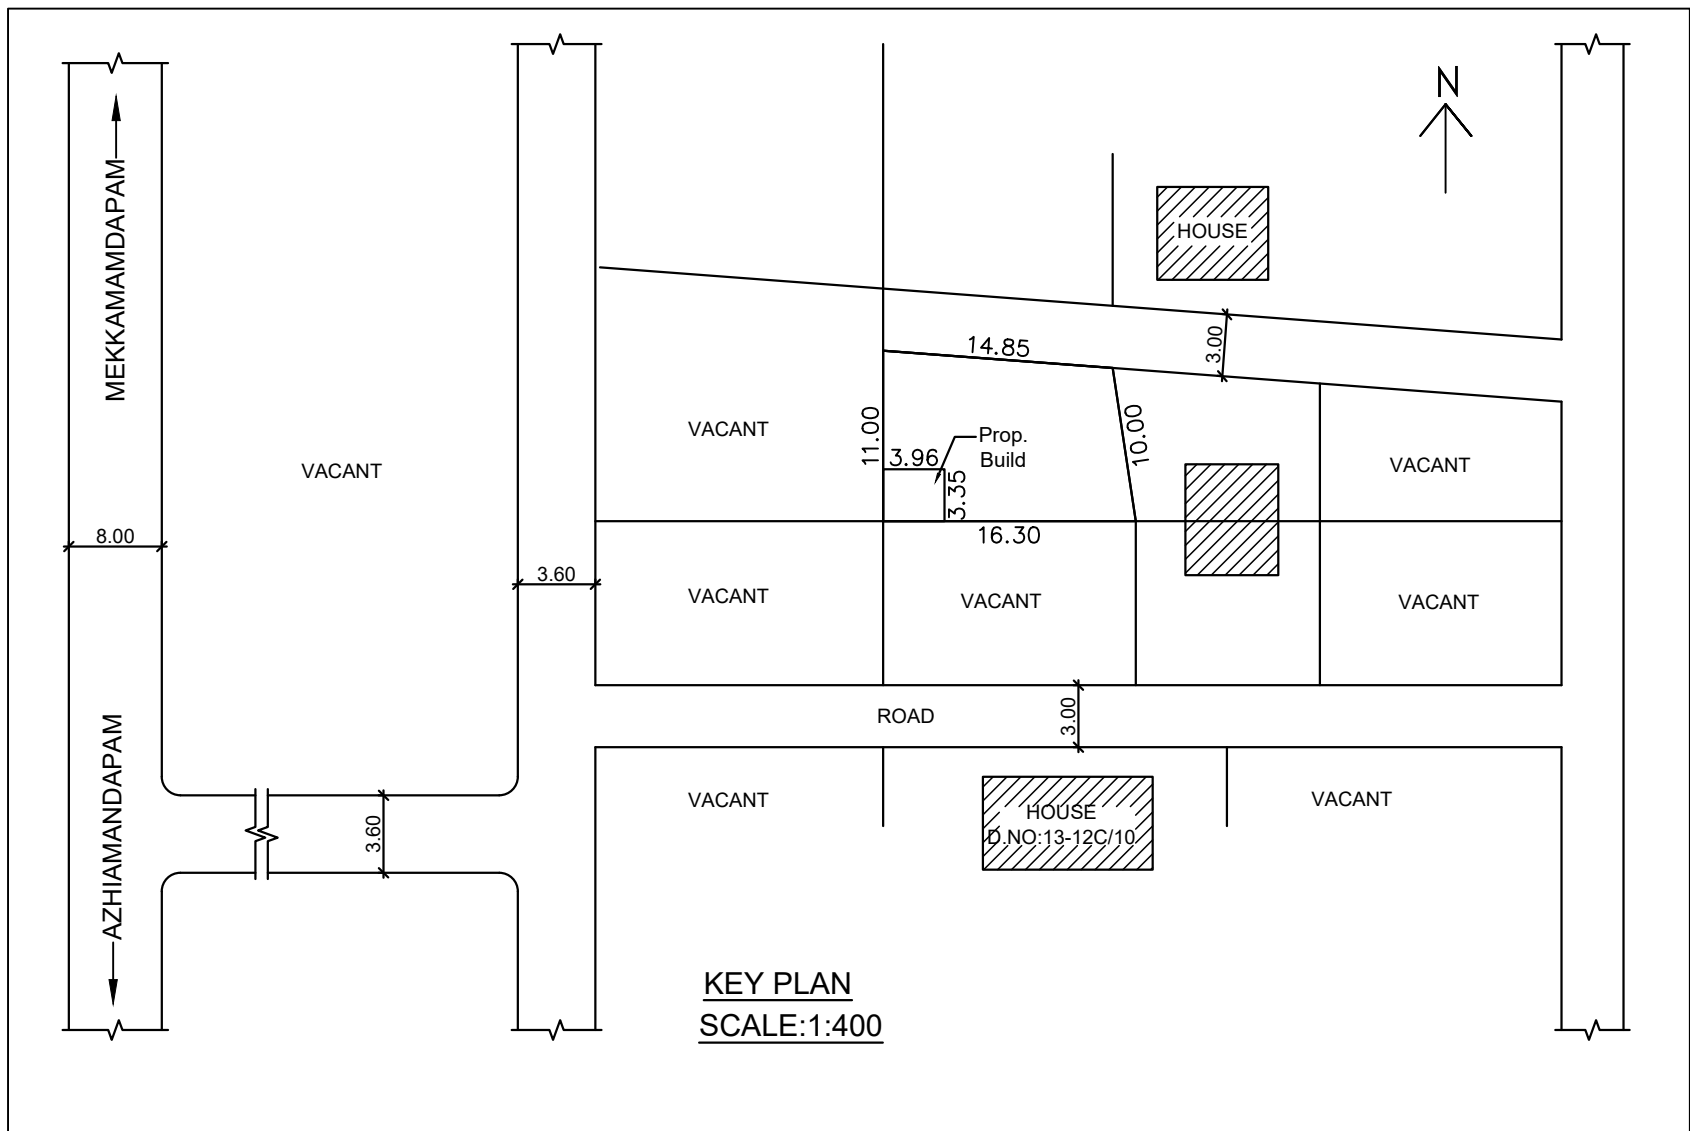
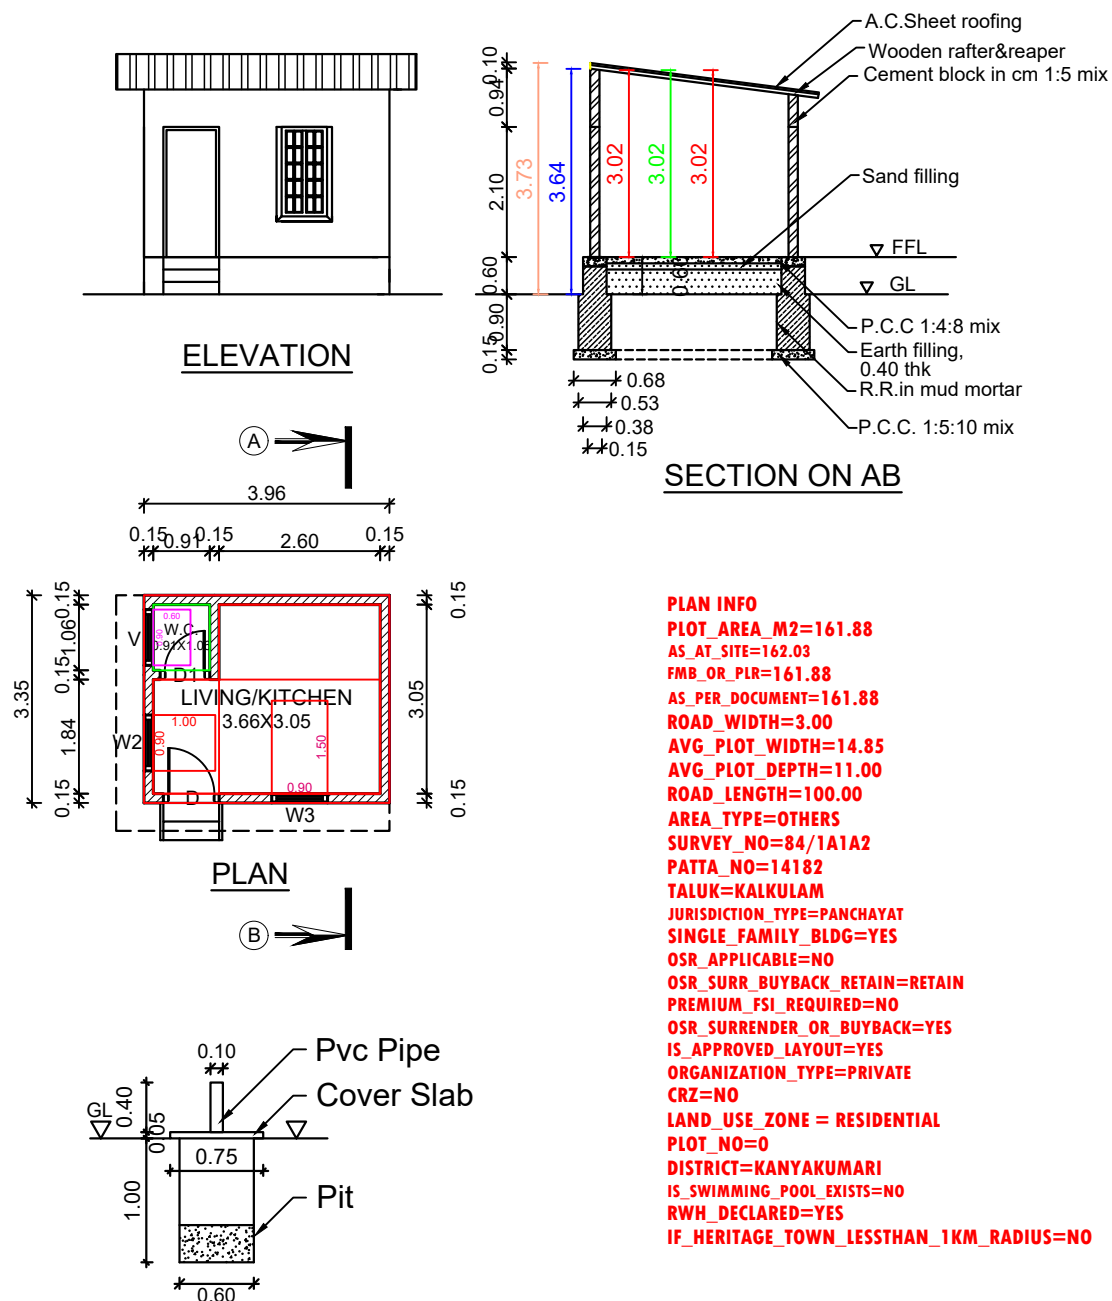


PLAN SHOWING THE PROPOSED CONSTRUCTION OF A A.C.SHEET ROOF RESIDENTIAL BUILDING
AT PULLUVILAI,PANANKALAVILAI IN RE.SY.NO: 84 / 1A1A2 OF THUCKALAY VILLAGE,
VILAVOOR TOWN PANCHAYAT , KALKULAM TALUK, KANYAKUMARI DISTRICT.

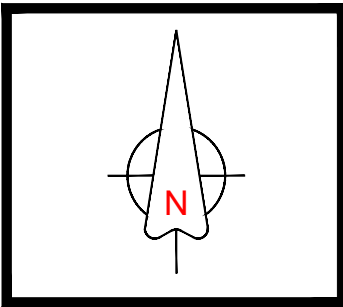

NAME OF APPLICANT :

Mr.R.ALBERT ,S/O Mr.RAJAIYAN ,
PULLUVILAI , PANANKALAVILAI ,
MULAGUMOODU P.O , K.K.DISTRICT .

AREA DETAILS - BUILDING		
PLINTH AREA		
Plinth Area	13.27 Sq.m	142.84 Sq.ft
Floor Area	10.85 Sq.m	116.79 Sq.ft
AREA DETAILS - PLOT		
Site Area	4.000 Cents	1.62 Are
	(161.880 Sq.m)	(1742.40 Sq.ft)
Vacant Area	148.61 Sq.m	1599.64 Sq.ft
F.S.I	13.27	161.88
PC	13.27	161.88

SCHEDULE OF JOINERIES		
REF	DESCRIPTION	SIZE
D	Door	0.90X2.10
D1	Door	0.80X2.10
W3	Window	1.50X1.50
W2	Window	0.90X1.50
KW2	Window	0.90X1.00
V	Ventilator	0.90X0.60

SCALE :	ALL DIMENSIONS	EDWG NO :
1:100	ARE IN METRE	0 0 0 2 0 1 2 6

R. Albert

APPLICANT

V. RETHNA MANI
LICENCED BUILDING SURVEYOR
LI. No: 331990, MOOLACHEL JN.
MEKKAMANDAPAM - 629 166
MOBIL: 9443157398
LICENSED SURVEYOR

